


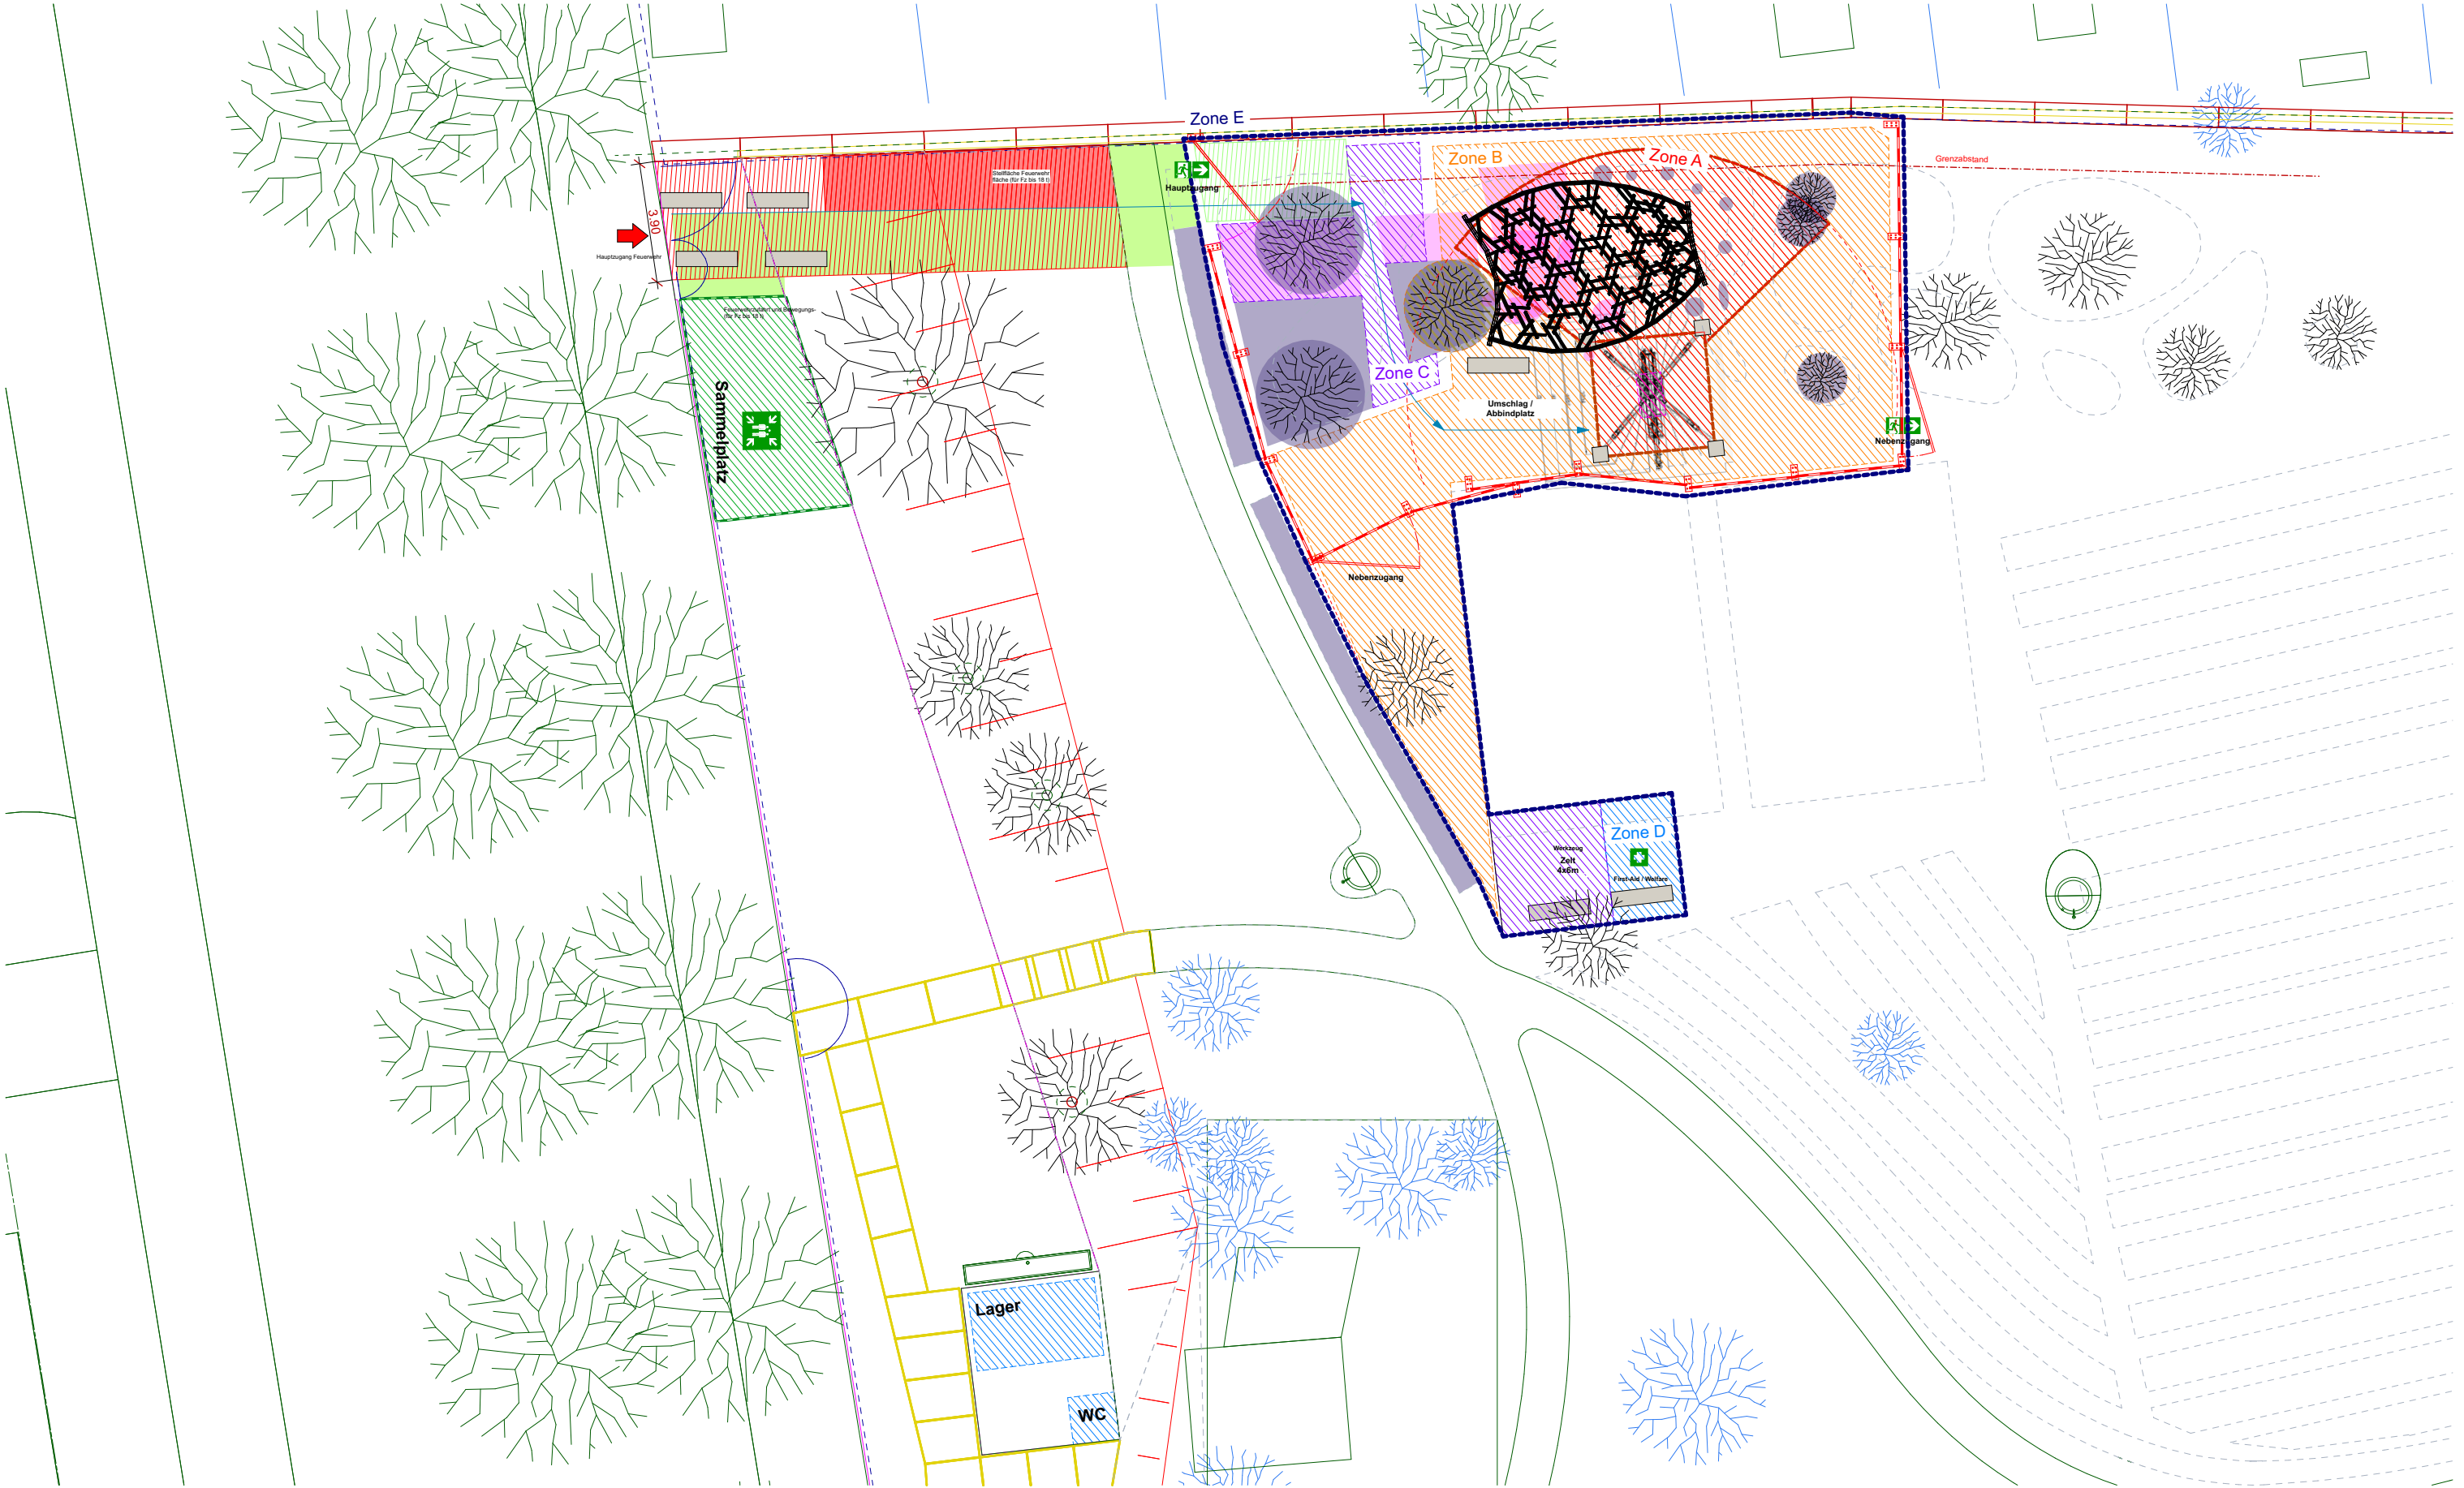

|                                                                                  |                                      |                             |                   |                                                          |             |        |            |
|----------------------------------------------------------------------------------|--------------------------------------|-----------------------------|-------------------|----------------------------------------------------------|-------------|--------|------------|
| BAUVORHABEN:<br>Pavillon Quartiergarten Hard<br>Bullingerstrasse 90, 8004 Zürich |                                      | AUFTRAGGEBER:<br>ETH Zürich |                   | PLANVERFASSER:<br>Gramazio Kohler Research<br>ETH Zürich |             |        |            |
| PLANNUMMER:<br>1.2                                                               | PLANTITEL:<br>Construction Site Plan | MASSSTAB:<br>1:100          | PLANGRÖSSE:<br>A3 | PROJEKTNUMMER:<br>409                                    | GEZEICHNET: | DATUM: | REVIDIERT: |

/Users/mac4ron/Documents/ETH/Coding Architecture/Focus Work/Baustellenplan\_29.pln

- Wichtige Pflanze Bestand

Bestehende Pflanze wird vor Baubeginn versetzt
- Hauptzugang Feuerwehr

Fluchtausgang

Sammelplatz

Medikit / Erstversorgung
- Feuerwehrezufahrt (für Fz bis 18 t)

Stellfläche Feuerweh (für Fz bis 18 t)

Fluchtweg

Freizuhaltende Fläche
- Zone A - Crane Operating Area

Zone B - Active Construction

Zone C - Tool & Material store

Zone D - Welfare / first aid

Zone E - Public Perimeter