


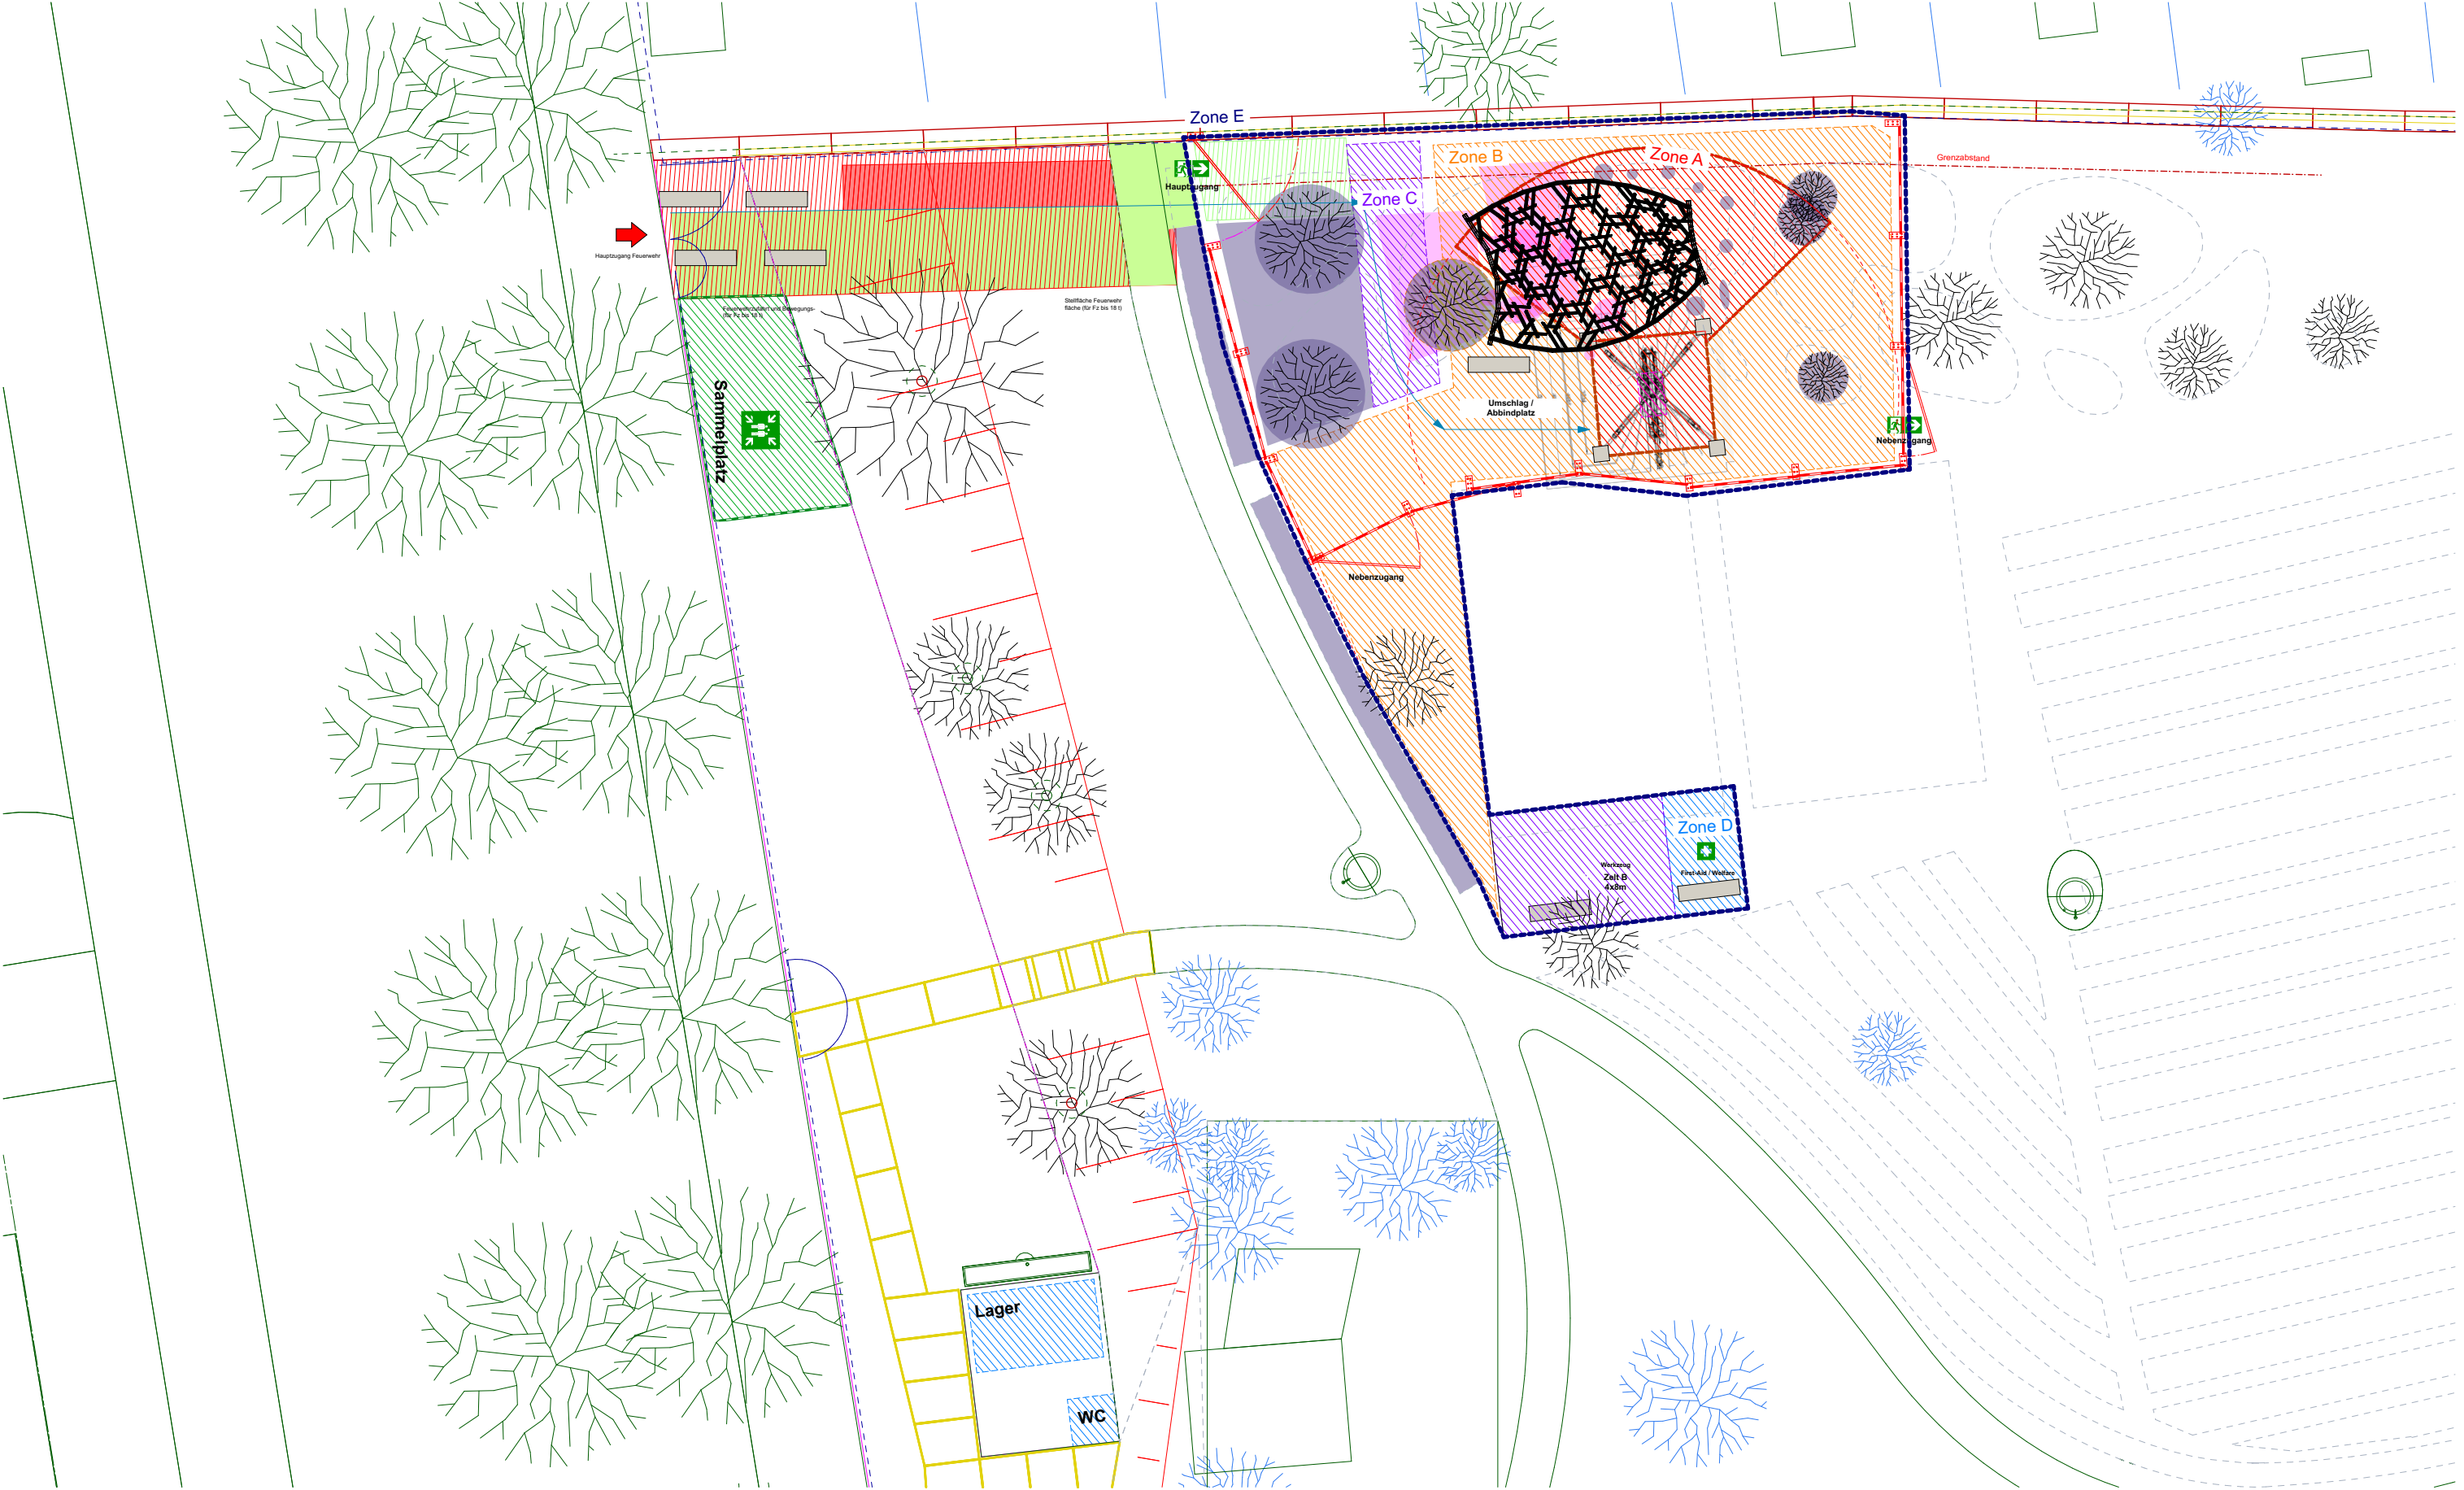

BAUVORHABEN: Pavillon Quartiergarten Hard Bullingerstrasse 90, 8004 Zürich		AUFTRAGGEBER: ETH Zürich		PLANVERFASSER: Gramazio Kohler Research ETH Zürich			
PLANNUMMER: 1.2	PLANTITEL: Construction Site Plan	MASSSTAB: 1:100	PLANGRÖSSE: A3	PROJEKTNUMMER: 409	GEZEICHNET:	DATUM:	REVIDIERT:

/Users/mac4ron/Documents/ETH/Coding Architecture/Focus Work/Baustellenplan_29.pln

- Wichtige Pflanze Bestand

Bestehende Pflanze wird vor Baubeginn versetzt
- Hauptzugang Feuerwehr

Fluchtausgang

Sammelplatz

Medikit / Erstversorgung
- Feuerwehruzufahrt (für Fz bis 18 t)

Stellfläche Feuerwehr (für Fz bis 18 t)

Fluchtweg

Freizuhaltende Fläche
- Zone A - Crane Operating Area

Zone B - Active Construction

Zone C - Tool & Material store

Zone D - Welfare / first aid

Zone E - Public Perimeter